


Occupation du domaine public : terrasse

Établissement fictif n° 1, 256 Place Saint-Léger

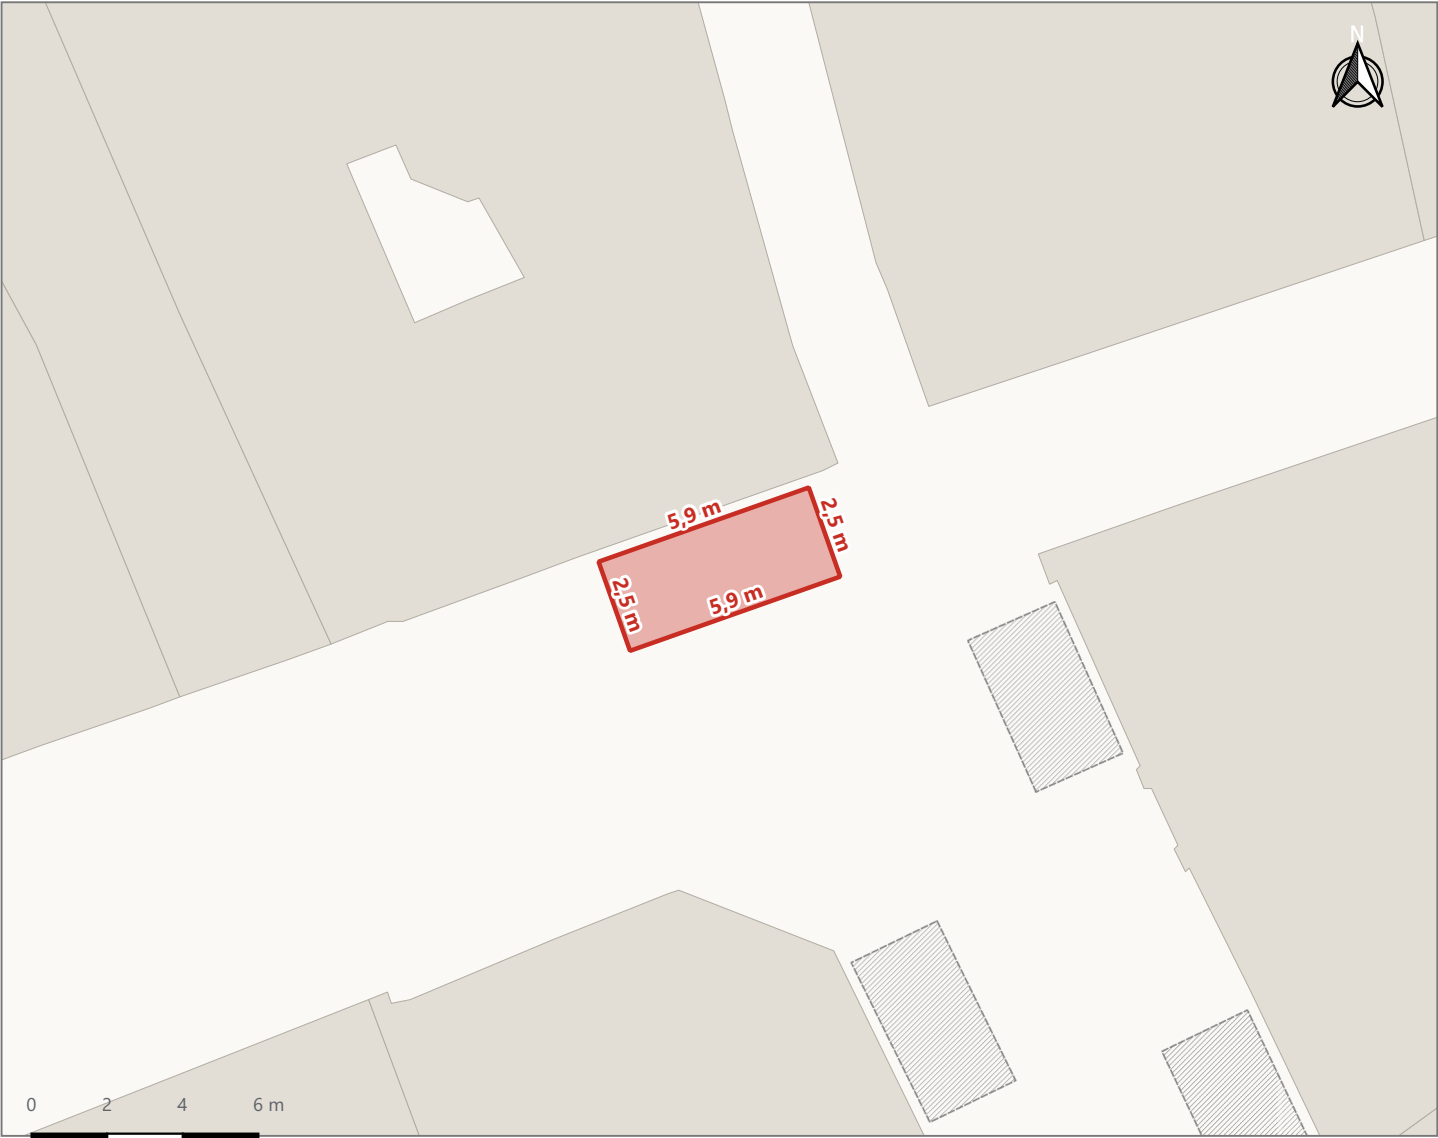

Caractéristiques de l'autorisation

Référence	OCC-2026-001
Type	Terrasse ouverte
Surface autorisée	14,8 m ²
Période	du 01/04/2026 au 31/10/2026
Statut	Autorisée
Voie	Place Saint-Léger (secteur piétonnier)

Situation



Emprise autorisée

Bâti

Autre terrasse

3,50 m

Cote en mètres

Le titulaire doit laisser libre un passage piéton de 1,40 m minimum. Tout mobilier hors de l'emprise est interdit.

Occupation du domaine public : terrasse

Établissement fictif n° 2, 254 Place Saint-Léger



Caractéristiques de l'autorisation

Référence	OCC-2026-002
Type	Terrasse ouverte
Surface autorisée	10,9 m²
Période	du 01/04/2026 au 31/10/2026
Statut	Autorisée
Voie	Place Saint-Léger (secteur piétonnier)

Situation



Emprise autorisée

Bâti

Autre terrasse


3,50 m

Cote en mètres

Le titulaire doit laisser libre un passage piéton de 1,40 m minimum. Tout mobilier hors de l'emprise est interdit.

Occupation du domaine public : terrasse


Établissement fictif n° 3, 255 Place Saint-Léger

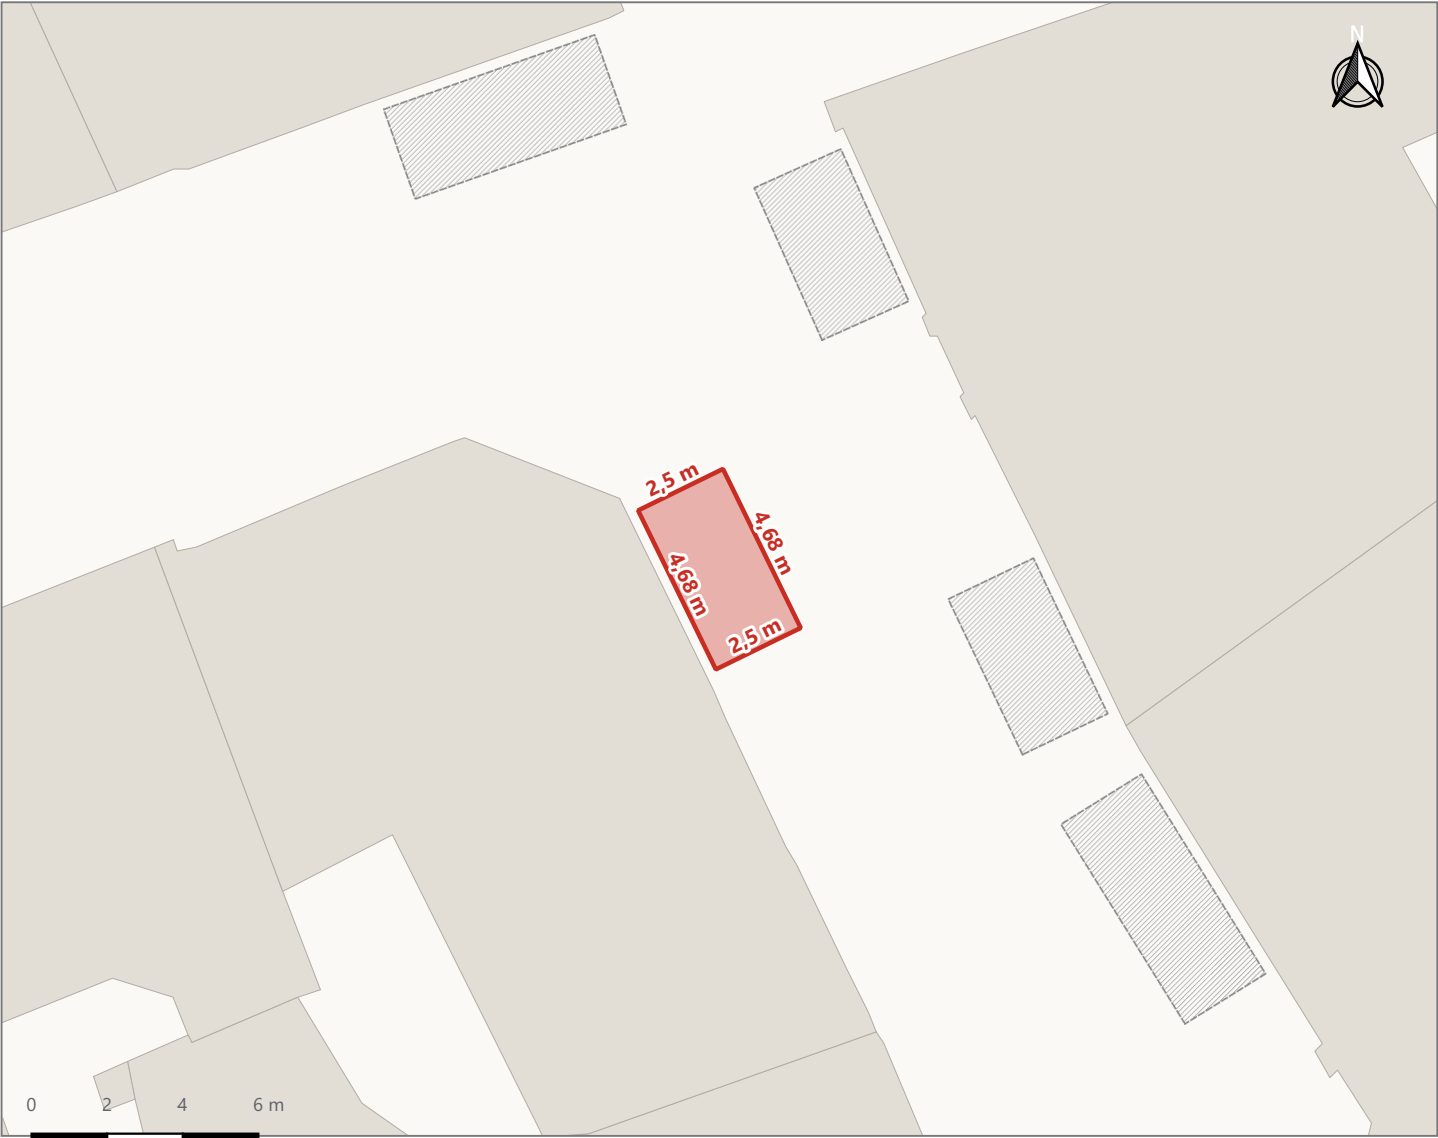

Caractéristiques de l'autorisation

Référence	OCC-2026-003
Type	Terrasse ouverte
Surface autorisée	11,7 m ²
Période	du 01/04/2026 au 31/10/2026
Statut	Autorisée
Voie	Place Saint-Léger (secteur piétonnier)

Situation

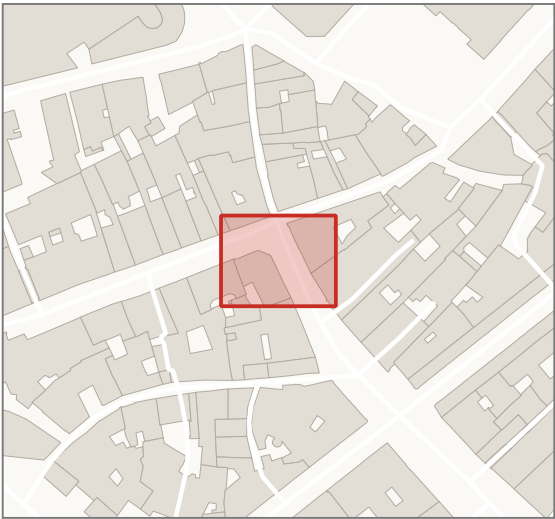

Emprise autorisée

Bâti


Autre terrasse

3,50 m Cote en mètres

Le titulaire doit laisser libre un passage piéton de 1,40 m minimum. Tout mobilier hors de l'emprise est interdit.

Occupation du domaine public : terrasse


Établissement fictif n° 4, 240 Place Saint-Léger

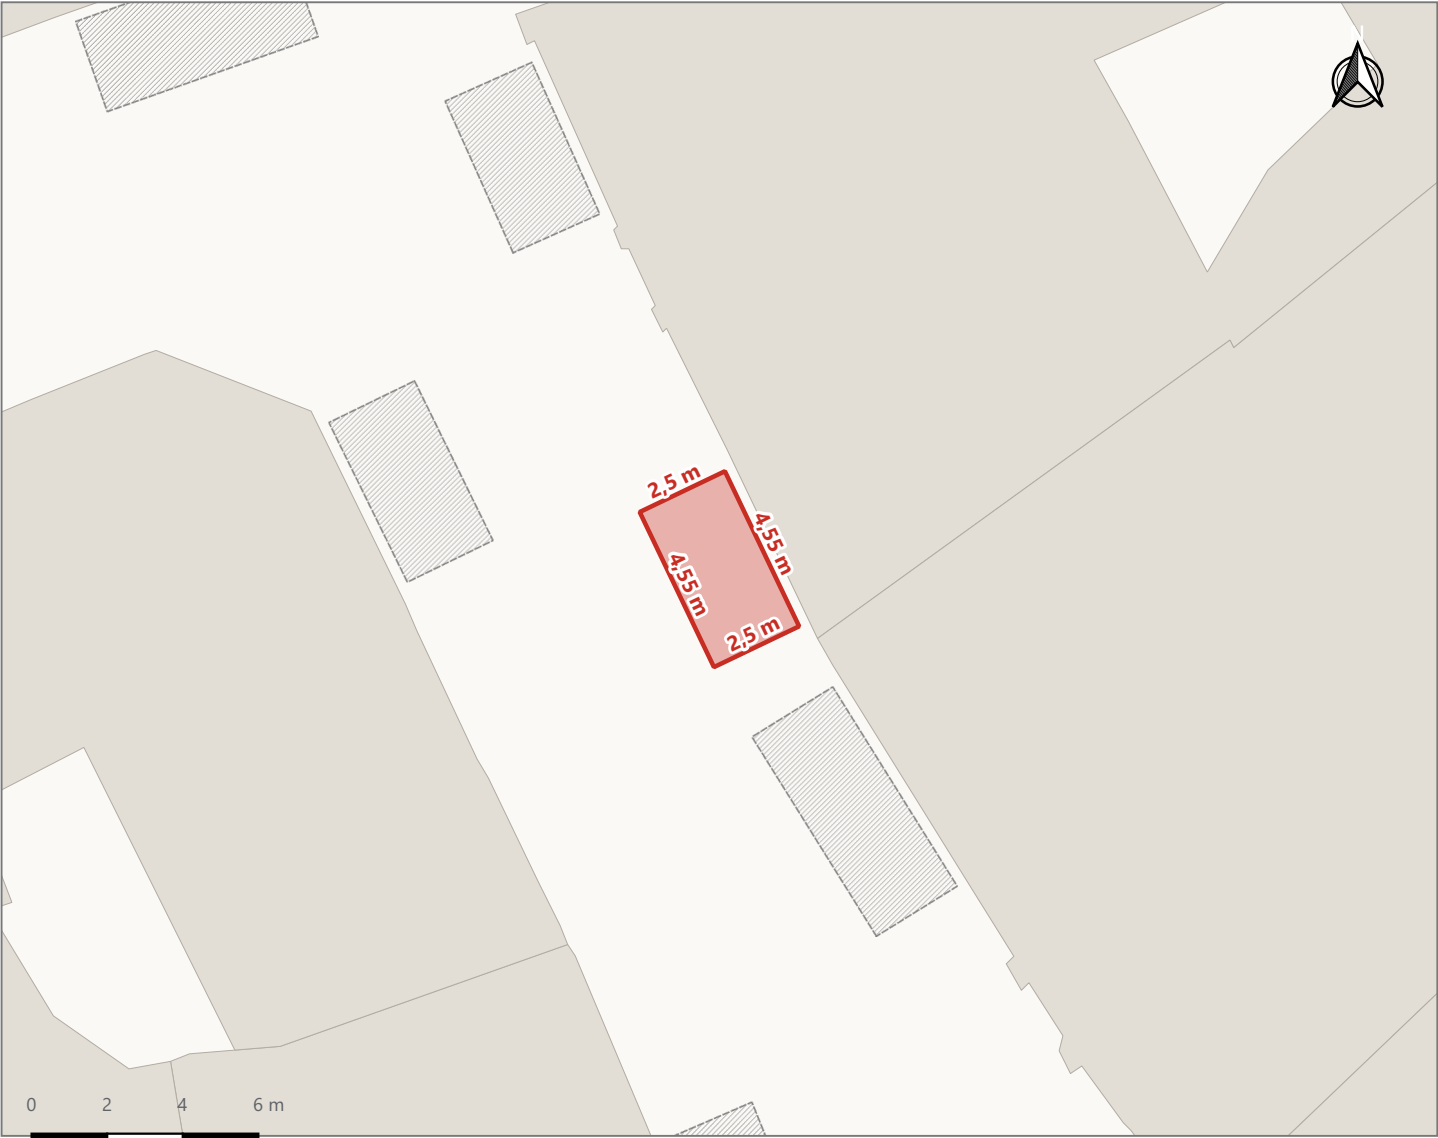

Caractéristiques de l'autorisation

Référence	OCC-2026-004
Type	Terrasse fermée
Surface autorisée	11,4 m ²
Période	du 01/04/2026 au 31/10/2026
Statut	Autorisée
Voie	Place Saint-Léger (secteur piétonnier)

Situation

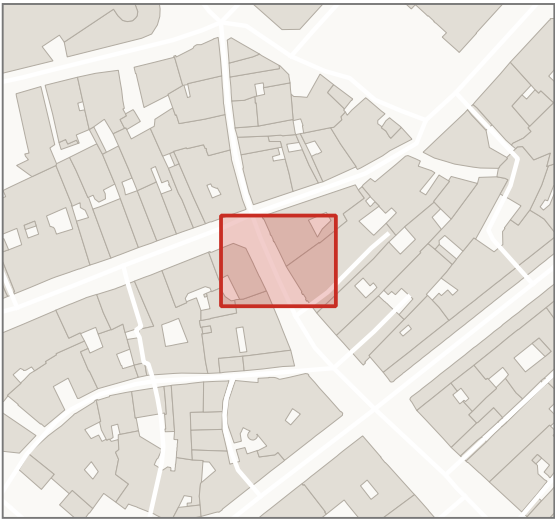

Emprise autorisée

Bâti

Autre terrasse

3,50 m Cote en mètres

Le titulaire doit laisser libre un passage piéton de 1,40 m minimum. Tout mobilier hors de l'emprise est interdit.

Occupation du domaine public : terrasse


Établissement fictif n° 5, 236 Place Saint-Léger



Caractéristiques de l'autorisation

Référence	OCC-2026-005
Type	Terrasse ouverte
Surface autorisée	15,5 m ²
Période	du 01/04/2026 au 31/10/2026
Statut	Autorisée
Voie	Place Saint-Léger (secteur piétonnier)

Situation

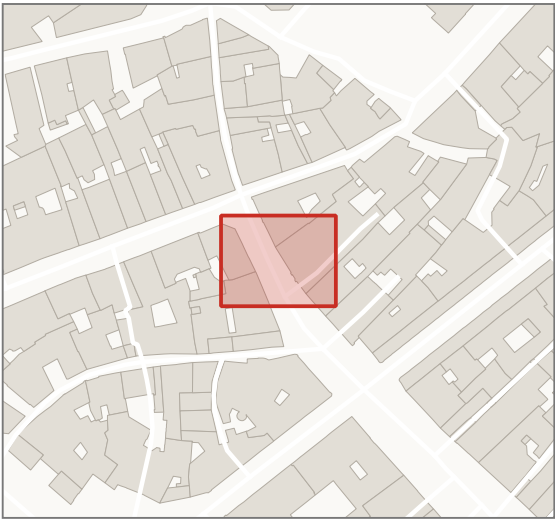

Emprise autorisée

Bâti

Autre terrasse


3,50 m

Cote en mètres

Le titulaire doit laisser libre un passage piéton de 1,40 m minimum. Tout mobilier hors de l'emprise est interdit.

Occupation du domaine public : terrasse


Établissement fictif n° 6, 239 Place Saint-Léger

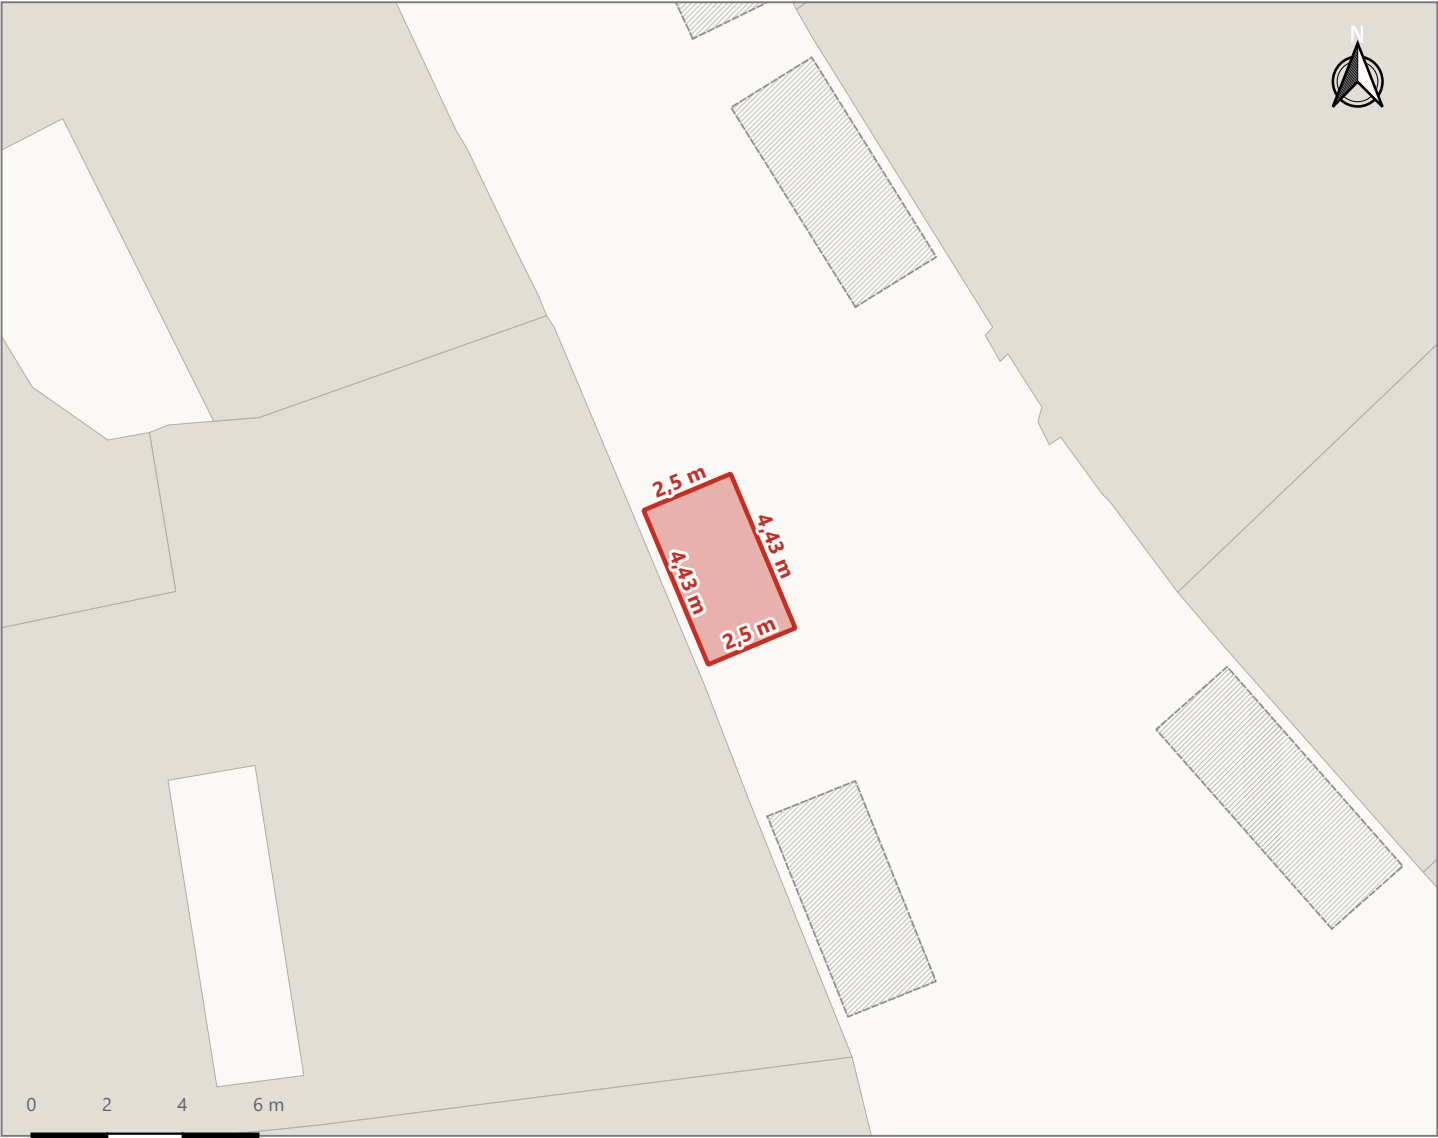

Caractéristiques de l'autorisation

Référence	OCC-2026-006
Type	Terrasse ouverte
Surface autorisée	11,1 m ²
Période	du 01/04/2026 au 31/10/2026
Statut	En instruction
Voie	Place Saint-Léger (secteur piétonnier)

Situation

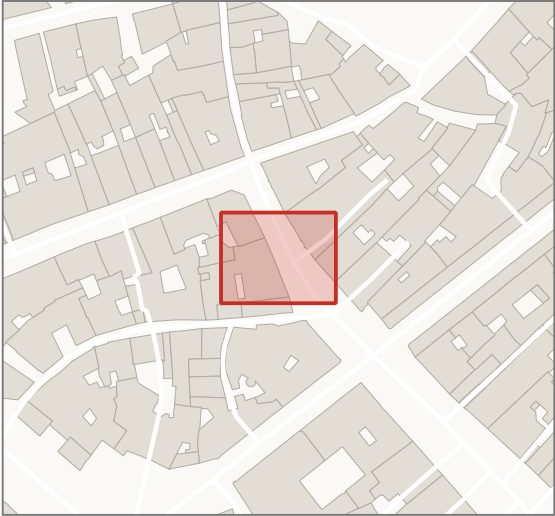

Emprise autorisée

Bâti

Autre terrasse

3,50 m

Cote en mètres

Le titulaire doit laisser libre un passage piéton de 1,40 m minimum. Tout mobilier hors de l'emprise est interdit.

Occupation du domaine public : terrasse


Établissement fictif n° 7, 216 Place Saint-Léger



Caractéristiques de l'autorisation

Référence	OCC-2026-007
Type	Terrasse ouverte
Surface autorisée	17,5 m ²
Période	du 01/04/2026 au 31/10/2026
Statut	Autorisée
Voie	Place Saint-Léger (secteur piétonnier)

Situation

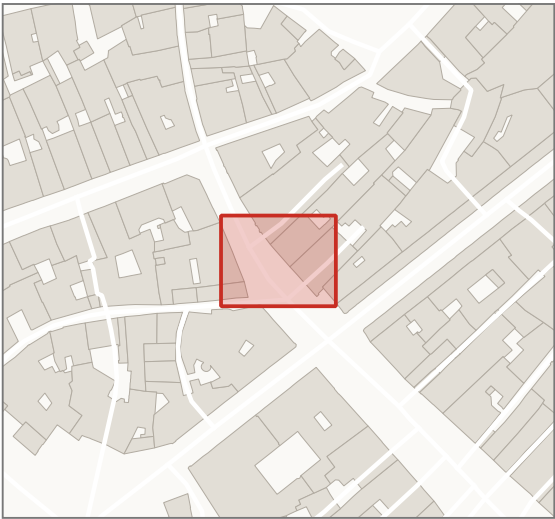

Emprise autorisée

Bâti

Autre terrasse


3,50 m

Cote en mètres

Le titulaire doit laisser libre un passage piéton de 1,40 m minimum. Tout mobilier hors de l'emprise est interdit.

Occupation du domaine public : terrasse


Établissement fictif n° 8, 225 Place Saint-Léger

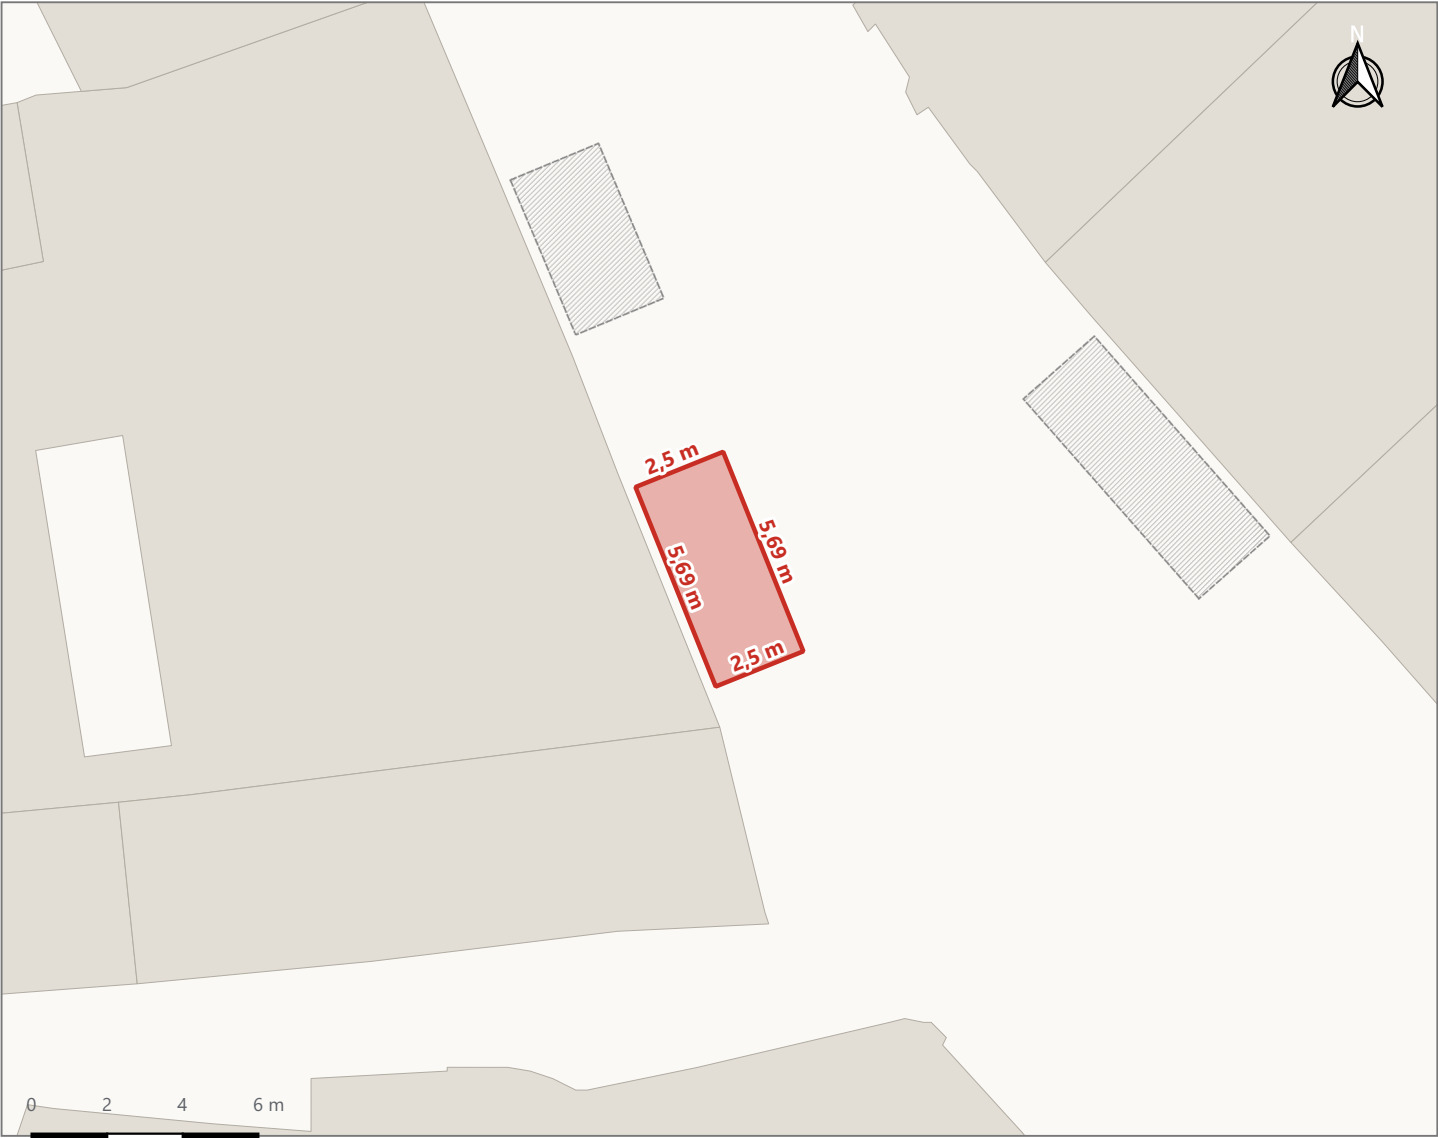

Caractéristiques de l'autorisation

Référence	OCC-2026-008
Type	Terrasse ouverte
Surface autorisée	14,2 m ²
Période	du 01/04/2026 au 31/10/2026
Statut	Autorisée
Voie	Place Saint-Léger (secteur piétonnier)

Situation

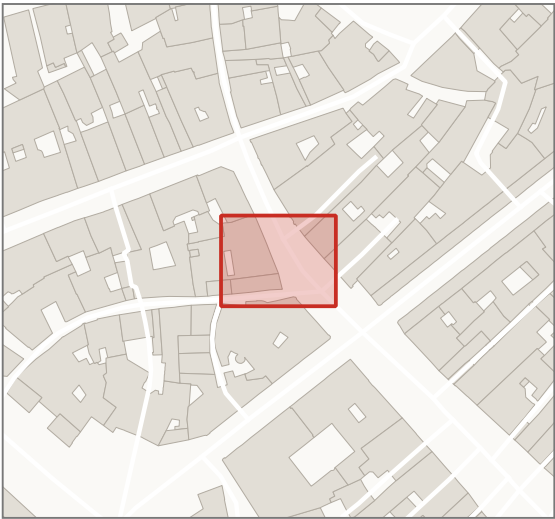

Emprise autorisée

Bâti

Autre terrasse


3,50 m

Cote en mètres

Le titulaire doit laisser libre un passage piéton de 1,40 m minimum. Tout mobilier hors de l'emprise est interdit.

Occupation du domaine public : terrasse


Établissement fictif n° 9, 39 Place Saint-Léger

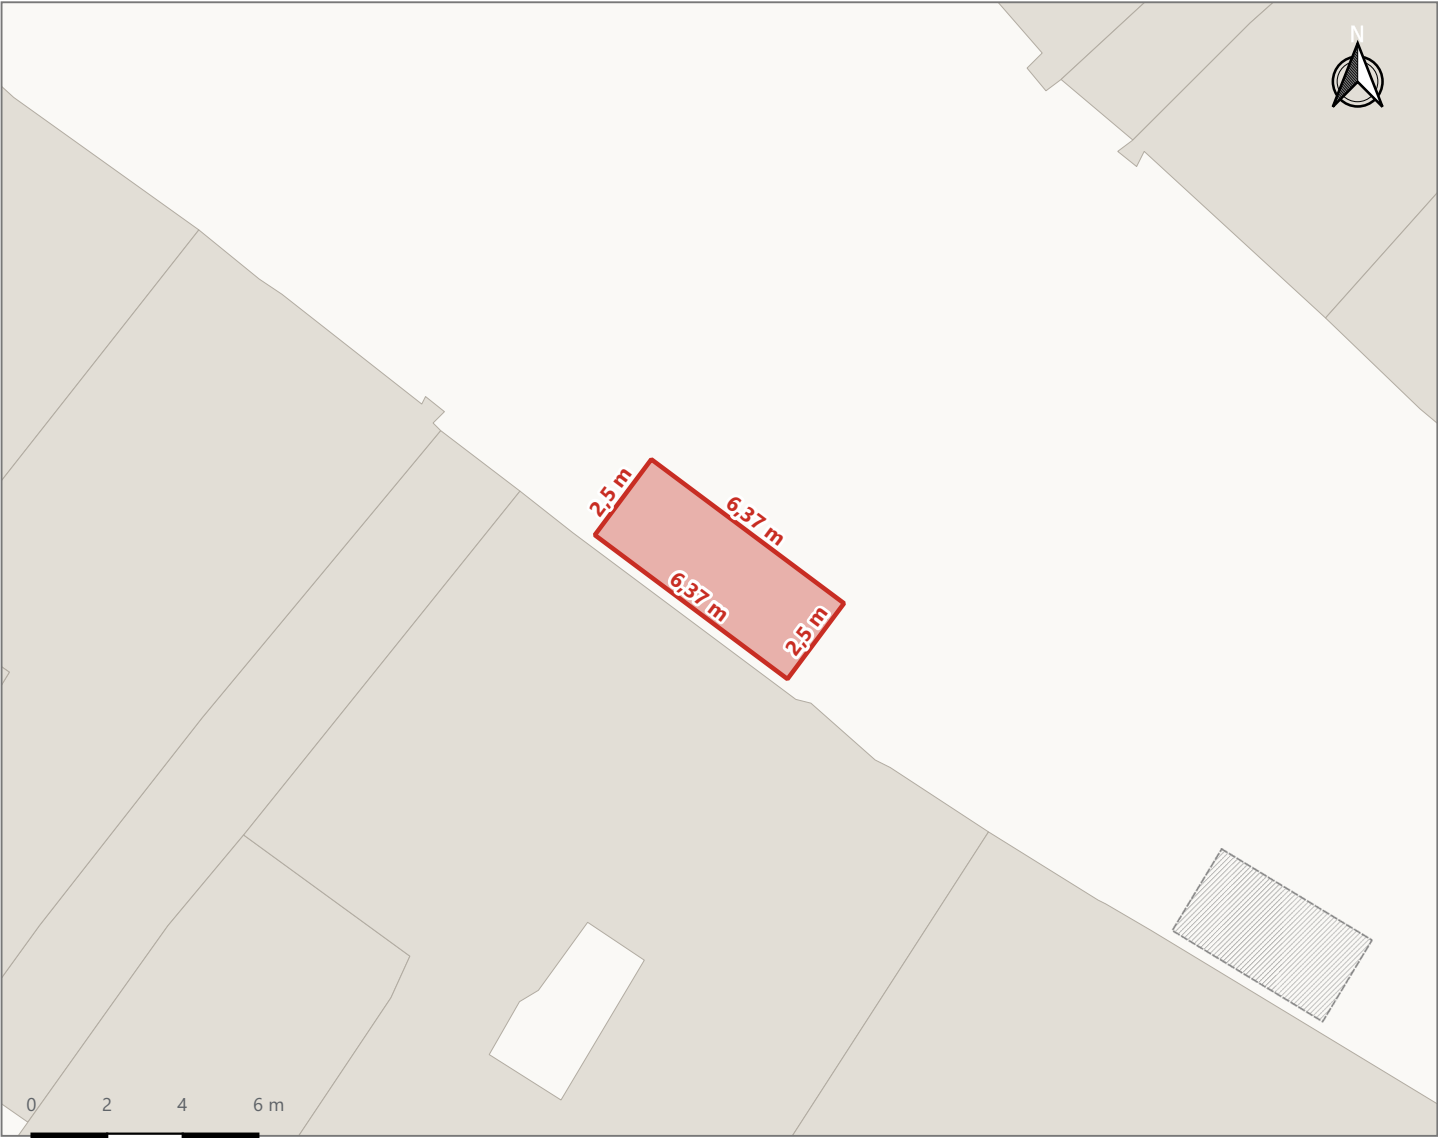

Caractéristiques de l'autorisation

Référence	OCC-2026-009
Type	Terrasse fermée
Surface autorisée	15,9 m²
Période	du 01/04/2026 au 31/10/2026
Statut	Autorisée
Voie	Place Saint-Léger (secteur piétonnier)

Situation

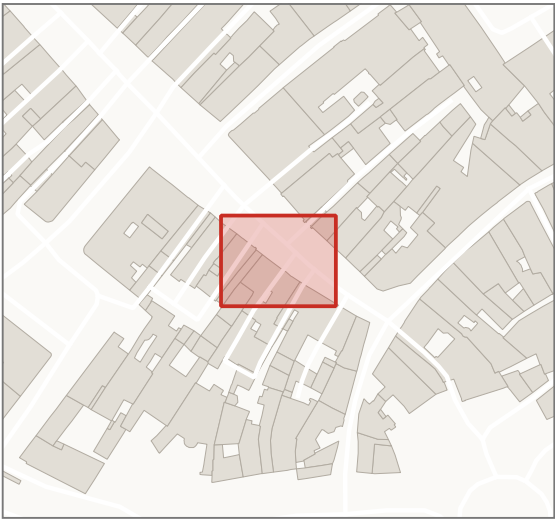

Emprise autorisée

Bâti


Autre terrasse

3,50 m Cote en mètres

Le titulaire doit laisser libre un passage piéton de 1,40 m minimum. Tout mobilier hors de l'emprise est interdit.

Occupation du domaine public : terrasse


Établissement fictif n° 10, 4 Place Saint-Léger

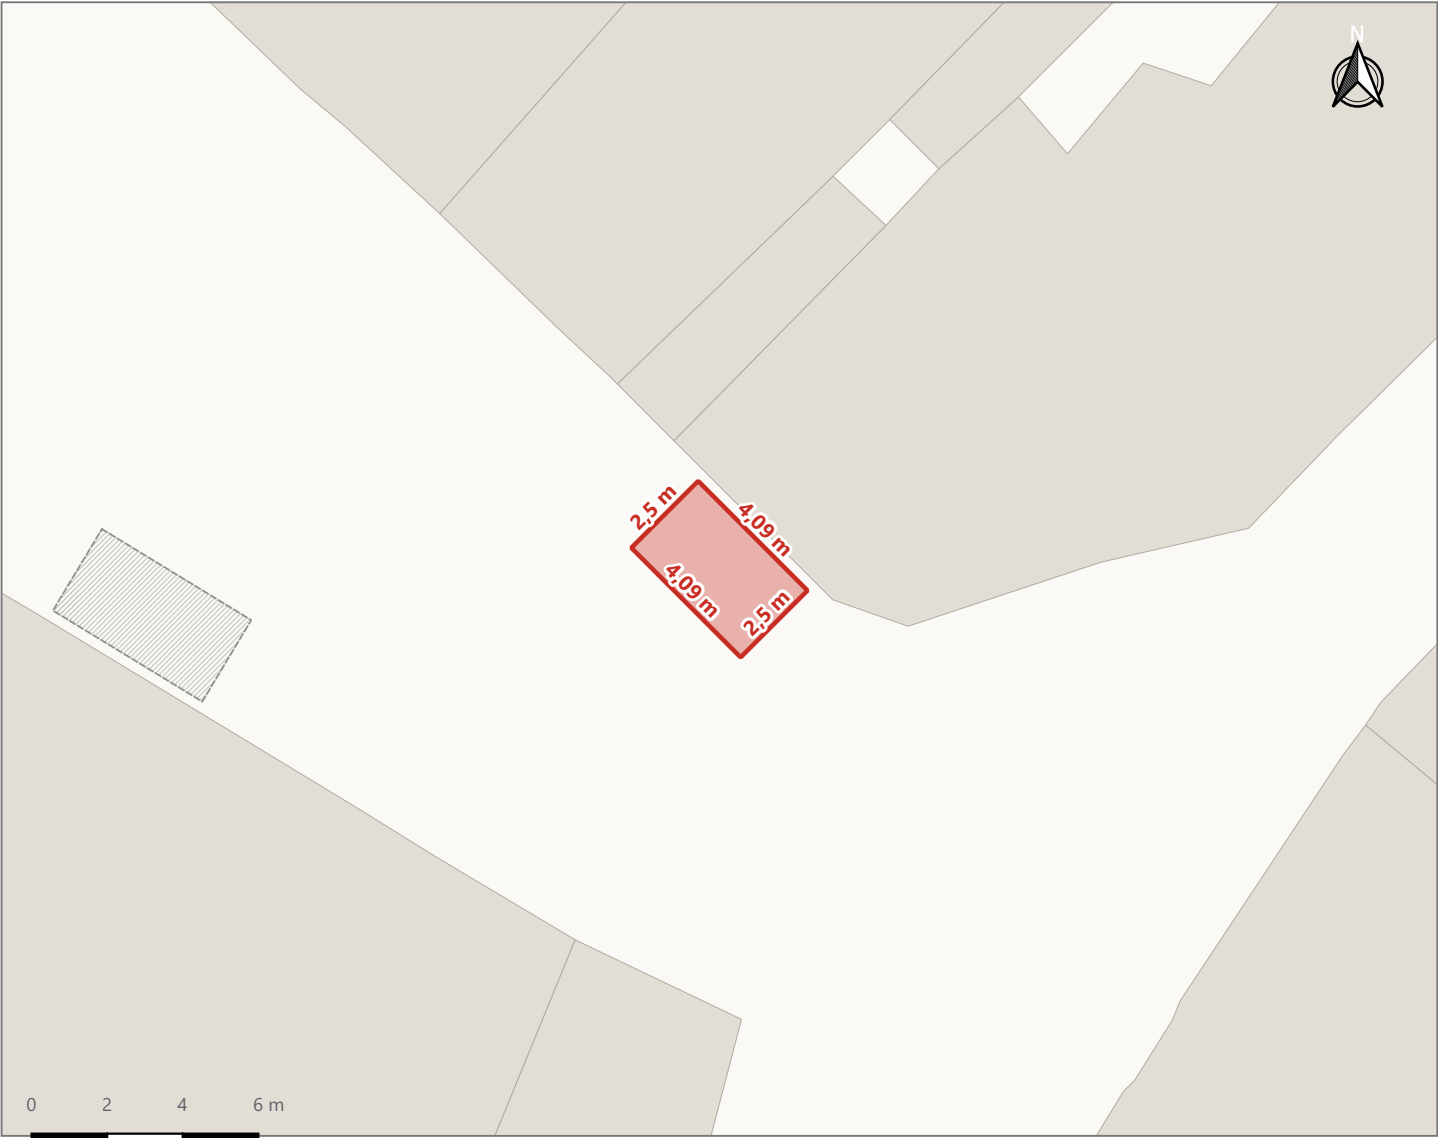

Caractéristiques de l'autorisation

Référence	OCC-2026-010
Type	Terrasse ouverte
Surface autorisée	10,2 m ²
Période	du 01/04/2026 au 31/10/2026
Statut	Autorisée
Voie	Place Saint-Léger (secteur piétonnier)

Situation

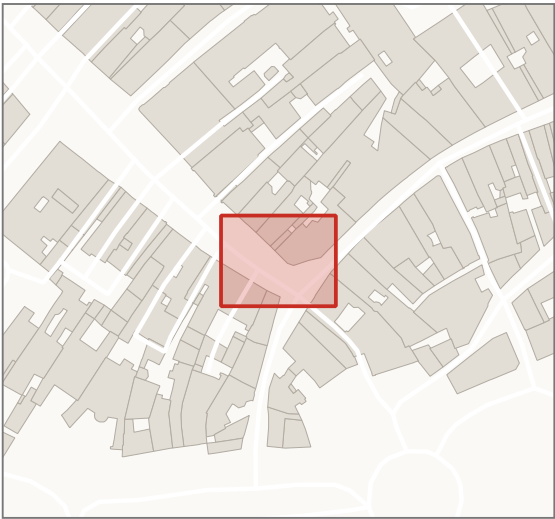

Emprise autorisée

Bâti

Autre terrasse


3,50 m

 Cote en mètres

Le titulaire doit laisser libre un passage piéton de 1,40 m minimum. Tout mobilier hors de l'emprise est interdit.

Occupation du domaine public : terrasse


Établissement fictif n° 11, 17 Place Saint-Léger

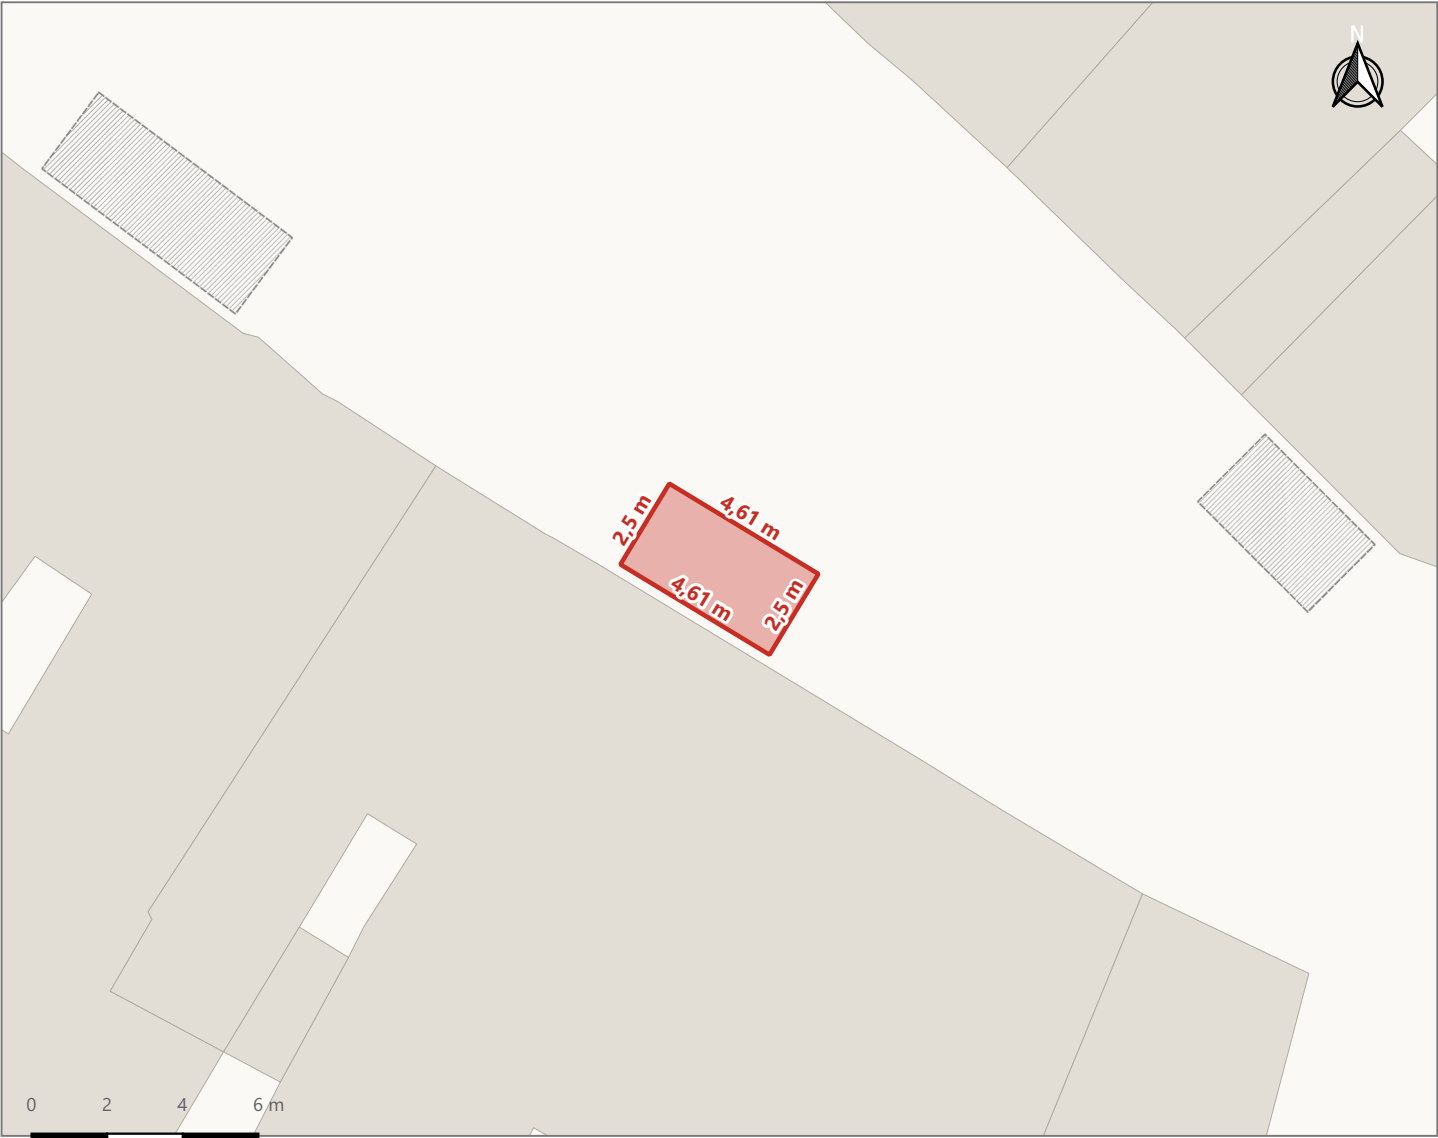

Caractéristiques de l'autorisation

Référence	OCC-2026-011
Type	Terrasse ouverte
Surface autorisée	11,5 m ²
Période	du 01/04/2026 au 31/10/2026
Statut	Autorisée
Voie	Place Saint-Léger (secteur piétonnier)

Situation

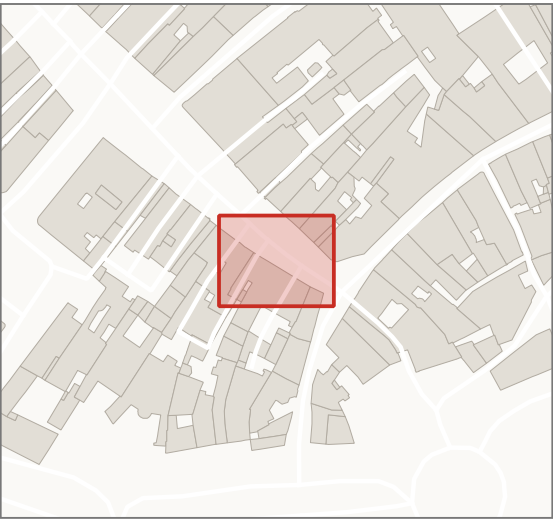

Emprise autorisée

Bâti

Autre terrasse

3,50 m Cote en mètres

Le titulaire doit laisser libre un passage piéton de 1,40 m minimum. Tout mobilier hors de l'emprise est interdit.